Quai Louis-Blanc - B.P. 1133 - 03103 MONTLUCON cedex - Tél. 04 70 02 51 30 - Fax 04 70 02 51 35 - mail. bgn-montlucon@bgn-sge.com

SOCIÉTÉ DE GÉOMÈTRES-EXPERTS

9 ter, Route de Chatel Guyon - B.P. 59 - 63202 RIOM cedex - Tél. 04 73 38 31 66 - Fax 04 73 38 31 56 - mail. bgn-riom@bgn-sge.com

6, Quai Henri ROBLIN 58300 DECIZE - Tél. 03 86 25 24 75 - Fax 04 70 46 88 41 - mail. bgn-vzeure@bgn-sge.com

Département de l'ALLIER

Commune d'AUROUER

Lotissement " La Croix Pruniaux "

Dossier consultation des entreprises

PLAN ASSAINISSEMENT ET RESEAUX

Indices	Dates	Modifications	Terrain	Bureau	Ch. projet
1	JUIN 2011	Consultation des entreprises	Y.D.	Y.D.	Y.D.

Echelle : 1/ 500e	81345	29 Juin 2011
Cadastre : Section B Parcelle 270		
Planimétrie : Système local Altimétrie : Système local		
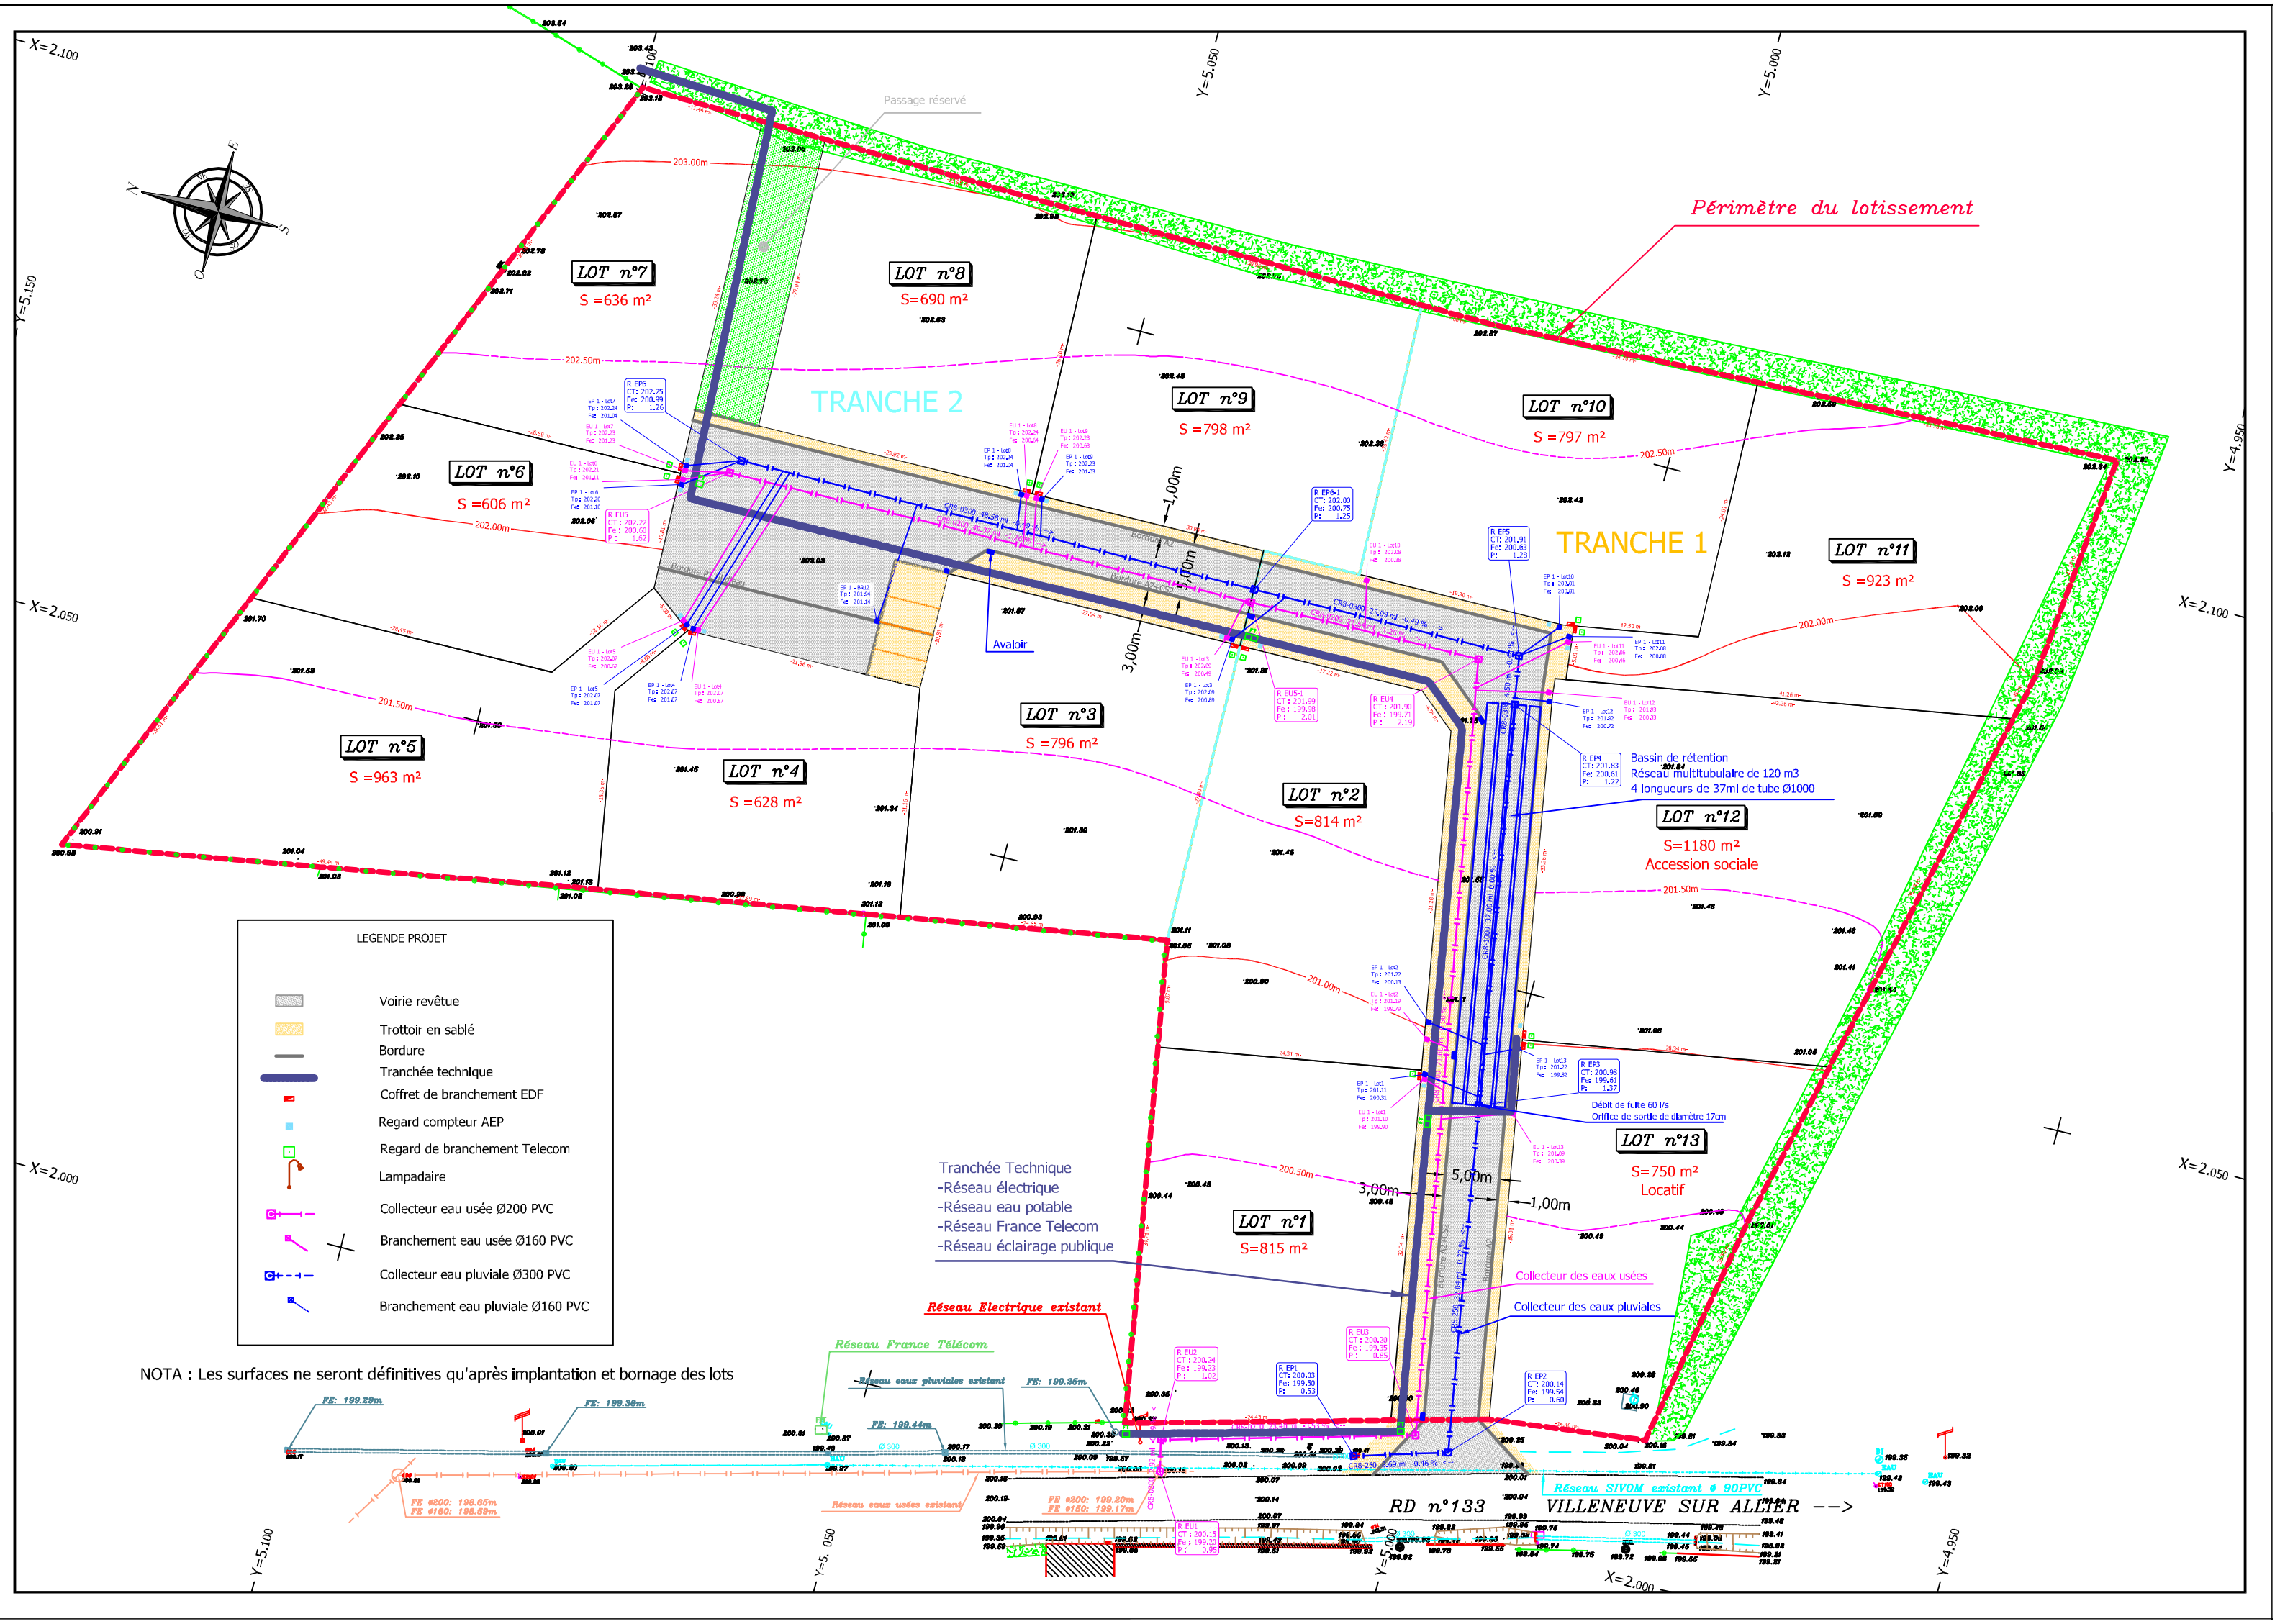
28, rue Ampère - B.P. 50 - 03402 YZEURE cedex - Tél. 04 70 46 72 29 - Fax 04 70 46 88 41 - mail. bgn-vzeure@bgn-sge.com
S.E.L.A.F.A au capital de 120 000 Euros - R.C.S. 323 014 902 - Ordre des Géomètres-Experts n° 93406
Siège Social : B.P. 1133 - 03103 MONTLUCON cedex - Site : www.bgn-sge.com